


BD 357350

DAFTAR ISIAN 206

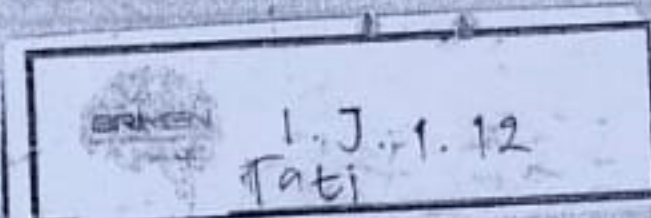

**BADAN PERTANAHAN NASIONAL  
REPUBLIK INDONESIA**

5993

Tati / Adung



**SERTIPIKAT  
(TANDA BUKTI HAK)**

KANTOR PERTANAHAN  
KABUPATEN / KOTA

**PURWAKARTA**

|   |   |   |   |   |   |   |   |   |   |   |   |   |   |   |   |   |   |   |
|---|---|---|---|---|---|---|---|---|---|---|---|---|---|---|---|---|---|---|
| 1 | 0 | • | 0 | 7 | • | 0 | 2 | • | 1 | 0 | • | 1 | • | 0 | 0 | 2 | 0 | 5 |
|---|---|---|---|---|---|---|---|---|---|---|---|---|---|---|---|---|---|---|

**BADAN PERTANAHAN NASIONAL  
REPUBLIK INDONESIA****SERTIPIKAT**HAK : **M I L I K** No. **00205**PROPINSI : **JAWA BARAT**KABUPATEN / KOTA : **PURWAKARTA**KECAMATAN : **BUNGURSARI**DESA / KELURAHAN : **KARANG MUKTI****KANTOR PERTANAHAN  
KABUPATEN / KOTA  
PURWAKARTA**

DAFTAR ISIAN 307

No.

DAFTAR ISIAN 208

No. 16685 / SIS / 2008

1 0 0 7 0 2 1 0 1 0 0 2 0 5

# PENDAFTARAN - PERTAMA

Halaman :

|   |   |
|---|---|
| <p>a) HAK : MILIK</p> <p>No. : 00205</p> <p>Desa / Kel. : Karang Mukti</p> <p>Tgl. berakhirnya hak :</p>   | <p>d) NAMA PEMEGANG HAK</p> <p><b>ADUNG bin NIMONG</b></p> <p>Tanggal lahir / akta pendirian :</p>   |
| <p>b) NIB : 10.07.02.10.00346</p> <p>Letak Tanah</p> <p>Kampung Sukamulya 03 / 02</p>   | <p>10-11-1967</p>   |
| <p>c) ASAL HAK</p> <p>1. Konversi / Pengakuan Hak</p> <p>2. Pemberian hak</p> <p>3. Pemecahan / Pemisahan / Penggabungan bidang</p>   | <p>g) PEMBUKUAN</p> <p>Purwakarta, Tgl. 07-11-2008</p> <p>An. Kepala Kantor Pertanahan Kabupaten / Kota</p> <p>Purwakarta</p> <p>Ketua Panitia Ajudikasi</p> <p>Nomor : 1007-03</p> <p>td</p>   |
| <p>d) DASAR PENDAFTARAN</p> <p>1. Daftar Isian 202</p> <p>Tgl. 27-10-2008</p> <p>No. 17/BA/2008</p> <p>2. Surat Keputusan</p> <p>Tgl.</p> <p>No.</p> <p>3. Permohonan Pemecahan / Pemisahan / Penggabungan bidang</p> <p>Tgl.</p> <p>No.</p> | <p></p> <p><u>H. KOSASIH, SH.</u></p> <p>NIP. 010 160 758</p> <p>h) PENERBITAN SERTIPIKAT</p> <p>Purwakarta, Tgl. 07-11-2008</p> <p>An. Kepala Kantor Pertanahan Kabupaten / Kota</p> <p>Purwakarta</p> <p>Ketua Panitia Ajudikasi</p> <p>Nomor : 1007-03</p> <p></p> <p><u>H. KOSASIH, SH.</u></p> <p>NIP. 010 160 758</p> |
| <p>e) SURAT UKUR</p> <p>Tgl. 05-11-2008</p> <p>No. 131 / Karang Mukti / 2008</p> <p>Luas. 1009 M<sup>2</sup></p> <p>Sembilan Sembilan Meter Persegi</p>                                                                                      | <p></p> <p><u>H. KOSASIH, SH.</u></p> <p>NIP. 010 160 758</p>   |
| <p>i) PENUNJUK</p> <p>Tanah Milik Adat SPPT No. 32.16.091.004.006-0055.0</p> <p>Surat Pernyataan Jual Beli Tanggal 08-09-2008</p>   |   |

Diukur oleh : PT.LENGGOGENI

Daftar Isian 302 tgl. No.

Daftar Isian 307 tgl. No.

Tanggal Penomoran Surat Ukur

UNTUK SERTIPIKAT

Purwakarta, 5 Nopember 2008

Purwakarta, 7 Nopember 2008

A.n. Kepala Seksi Survei, Pengukuran dan Pemetaan



NTP 010 160 758



NIP

Kantor Pertanahan  
Kabupaten / Kota  
PURWAKARTA  
Ketua Panitia Ajudikasi  
Nomor 1007-03  
ttd

H. KOSASHI, SH

010 160 758

|                  |              |
|------------------|--------------|
|                  | Pemisahan    |
| Lihat surat ukur | Penggabungan |
|                  | Pengganti    |

Nomor :

• Nomor hak :

| Dikeluarkan surat ukur |       | Luas | Nomor hak | Sisa luas |
|------------------------|-------|------|-----------|-----------|
| Tanggal                | Nomor |      |           |           |
|                        |       |      |           |           |

Sisanya diuraikan dalam surat ukur Nomor :

Nomor hak :

TESLAH GEOKAP

DAFTAR ISIAN 207

1 0 • 0 7 • 0 2 • 1 0 • 1 • 0 0 2 0 5

NIB : 10.07.02.10.00346

## SURAT UKUR

Nomor : 131 / Karang Mukti / 2008

### SEBIDANG TANAH TERLETAK DALAM

Propinsi : JAWA BARAT

Kabupaten / Kota : PURWAKARTA

Kecamatan : BUNGURSARI

Desa / Kelurahan : KARANG MUKTI - Kampung Sukamulya RT 03 / RW 02

Peta : Pendaftaran Nomor Peta Pendaftaran : 48.2-47.085-07-4

Lembar : 07-4 Kotak : D3

Keadaan Tanah : Sebidang Tanah Perumahan


Tanda-tanda batas : Patok Beton

Luas : 1009 m<sup>2</sup> (seribu sembilan meter persegi)

Penunjukan dan penetapan batas : Ditunjukkan oleh : ADUNG bin NIMONG (Pemilik)



SKALA 1 : 500

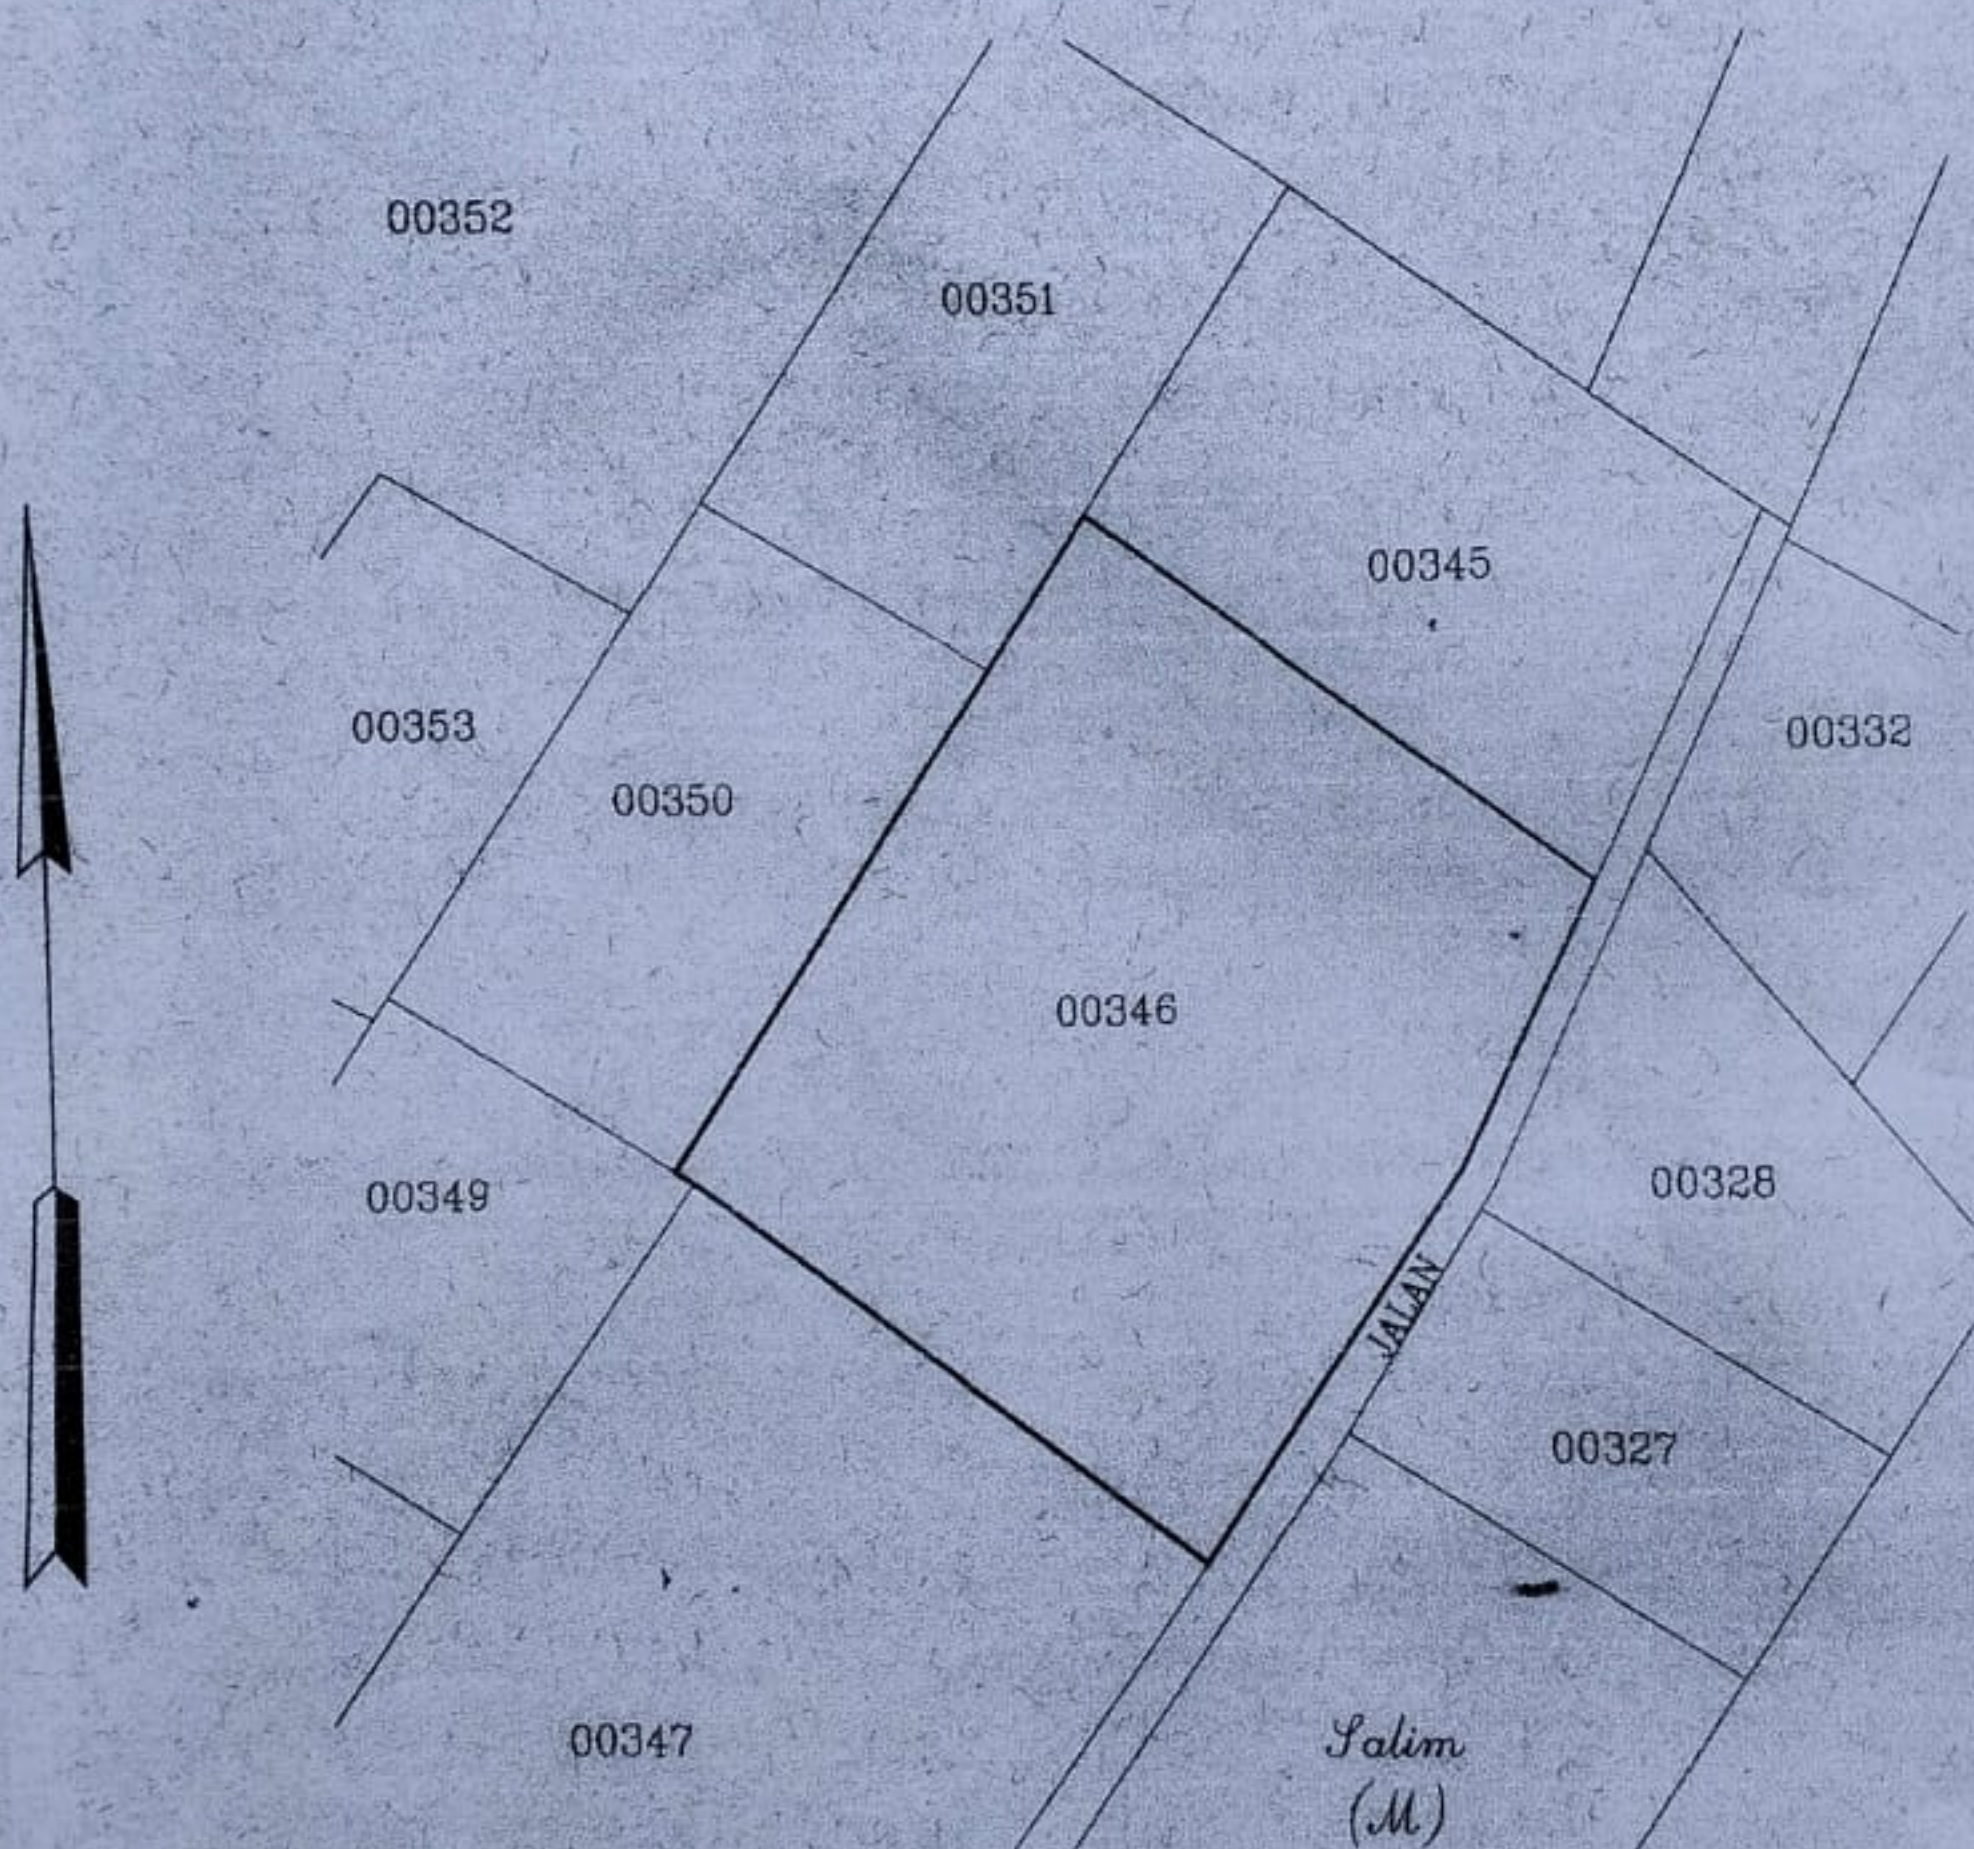

PENJELASAN : \_\_\_\_\_ batas tanah ini

# PENDAFTARAN PERALIHAN HAK, PEMBEBANAN DAN PENCATATAN LAINNYA

Halaman :

| Sebab perubahan,<br>Tanggal pendaftaran,<br>No. Daftar istan   | Nama yang berhak<br>dan<br>Pemegang hak lain-lainnya | Tanda tangan Kepala kantor<br>dan Cap Kantor |
|---|------------------------------------------------------|----------------------------------------------|
| <div data-bbox="140 799 872 949"> <div> <div> TELAH DIPERIKSA DAN SESUAI DENGAN<br/>DAFTAR DI KANTOR PERTANAHAN </div> <div> D. 303<br/>9590 </div> <div> TGL<br/>09/12 </div> <div> PARAF<br/>↓ </div> </div> </div> |                                                      |                                              |

